


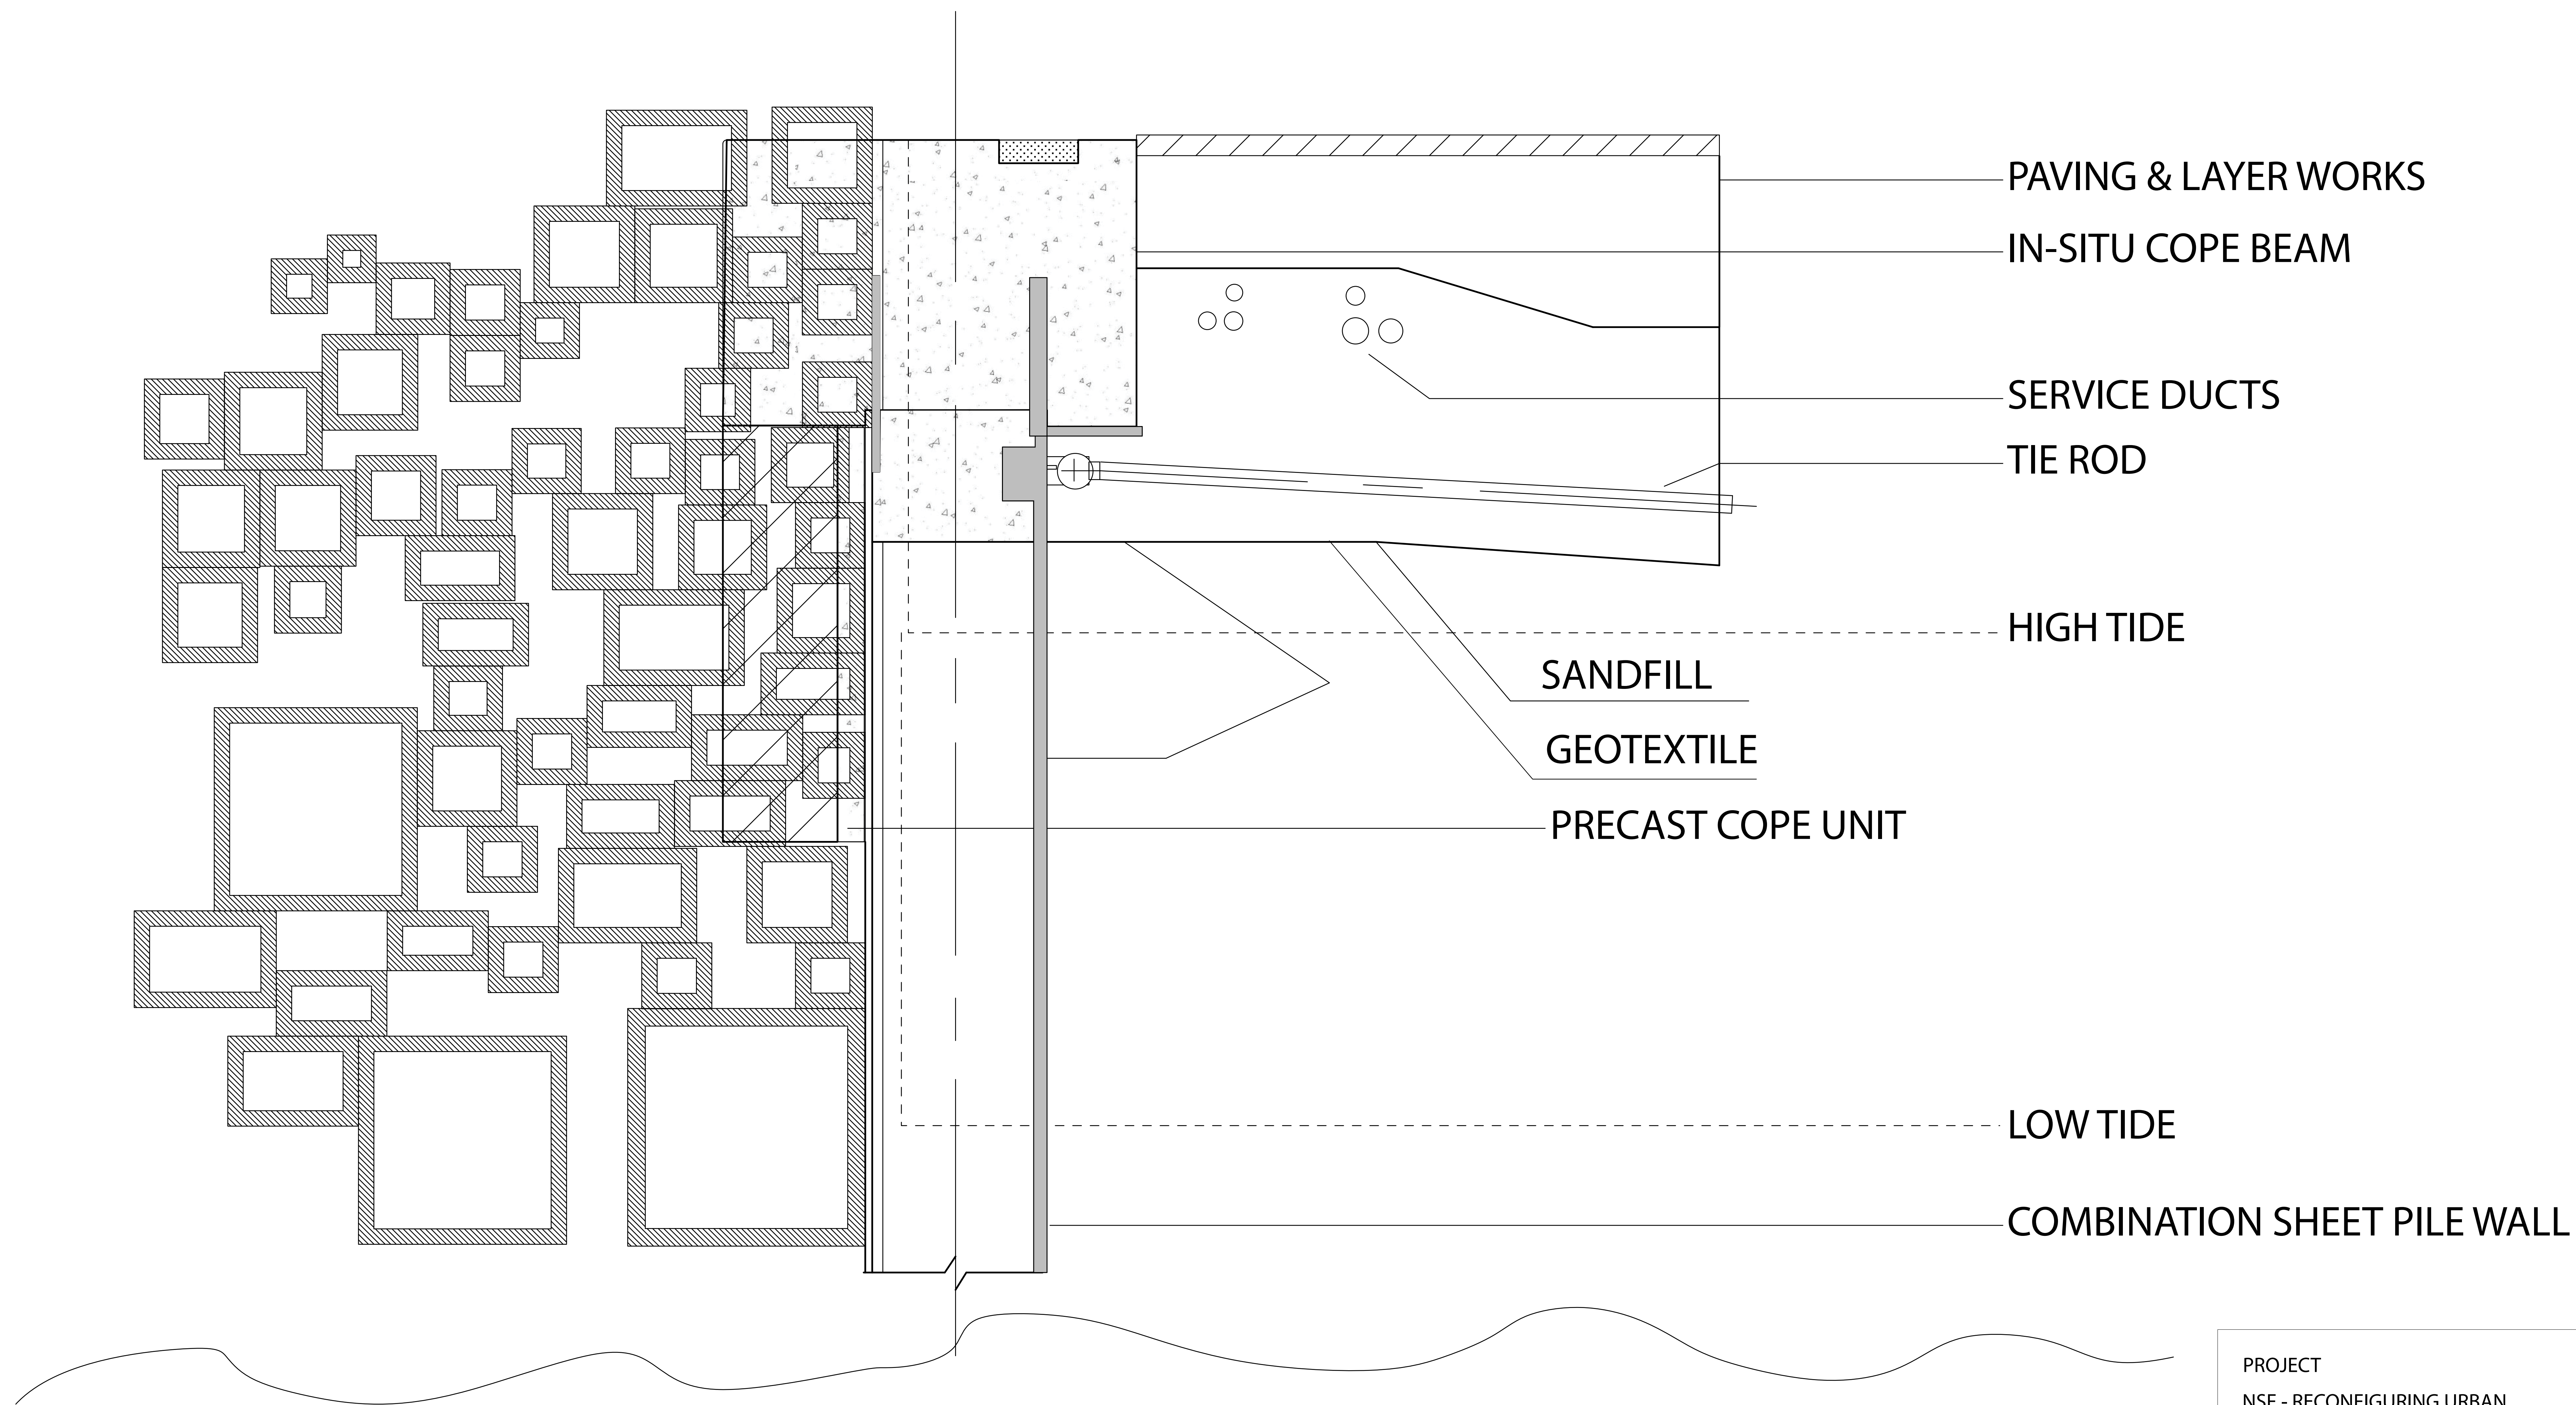

PAVING & LAYER WORKS

IN-SITU COPE BEAM

SERVICE DUCTS

TIE ROD

HIGH TIDE

SANDFILL

GEOTEXTILE

PRECAST COPE UNIT

LOW TIDE

COMBINATION SHEET PILE WALL

PROJECT NSF - RECONFIGURING URBAN SHORELINES FOR RESILIENCE NEW YORK, NY	
TITLE 3D PRINTED CONCRETE UNITS ARRAYED ALONG & ATTACHED TO SHEET FILM	
SCALE: 1.5" = 1"	
DATE: 3/21/2022	
	SK-01